


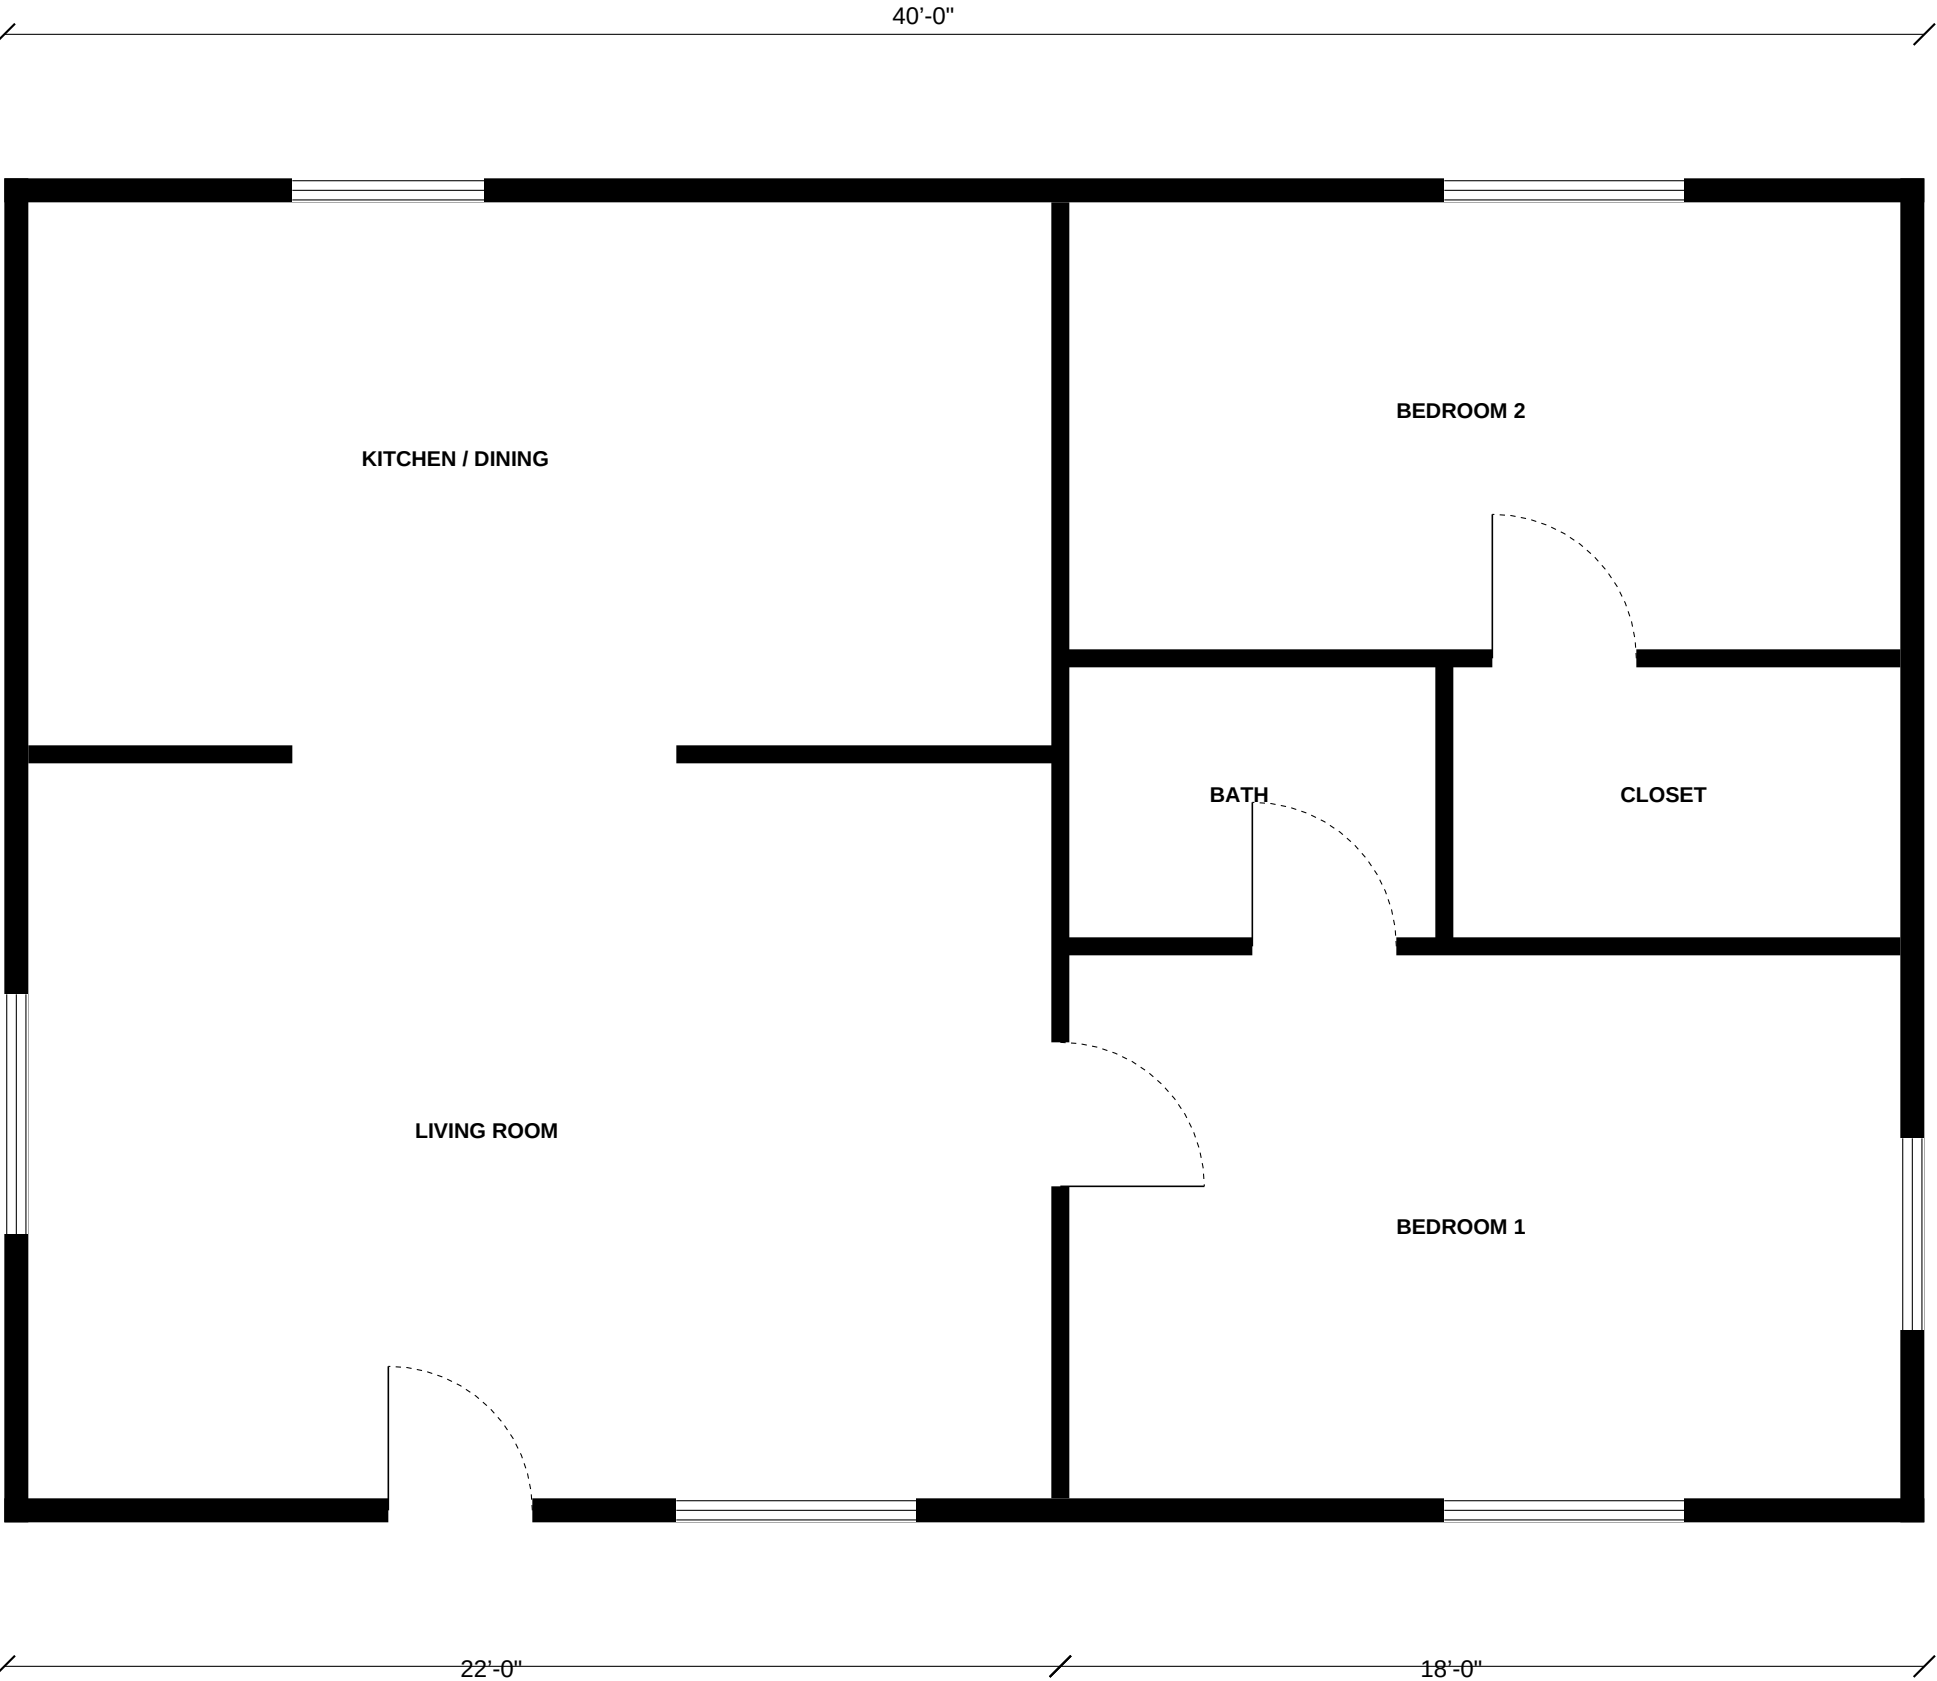

KORbuild


Planta de exemplo

CASA MODELO

1450 Elm St, Manchester, NH

FIRST FLOOR PLAN

SCALE: 1/4" = 1'-0"

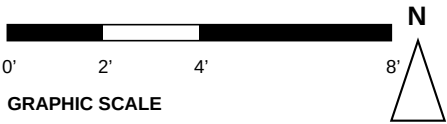

SHEET

A-101

Prototipo - planta ficticia